
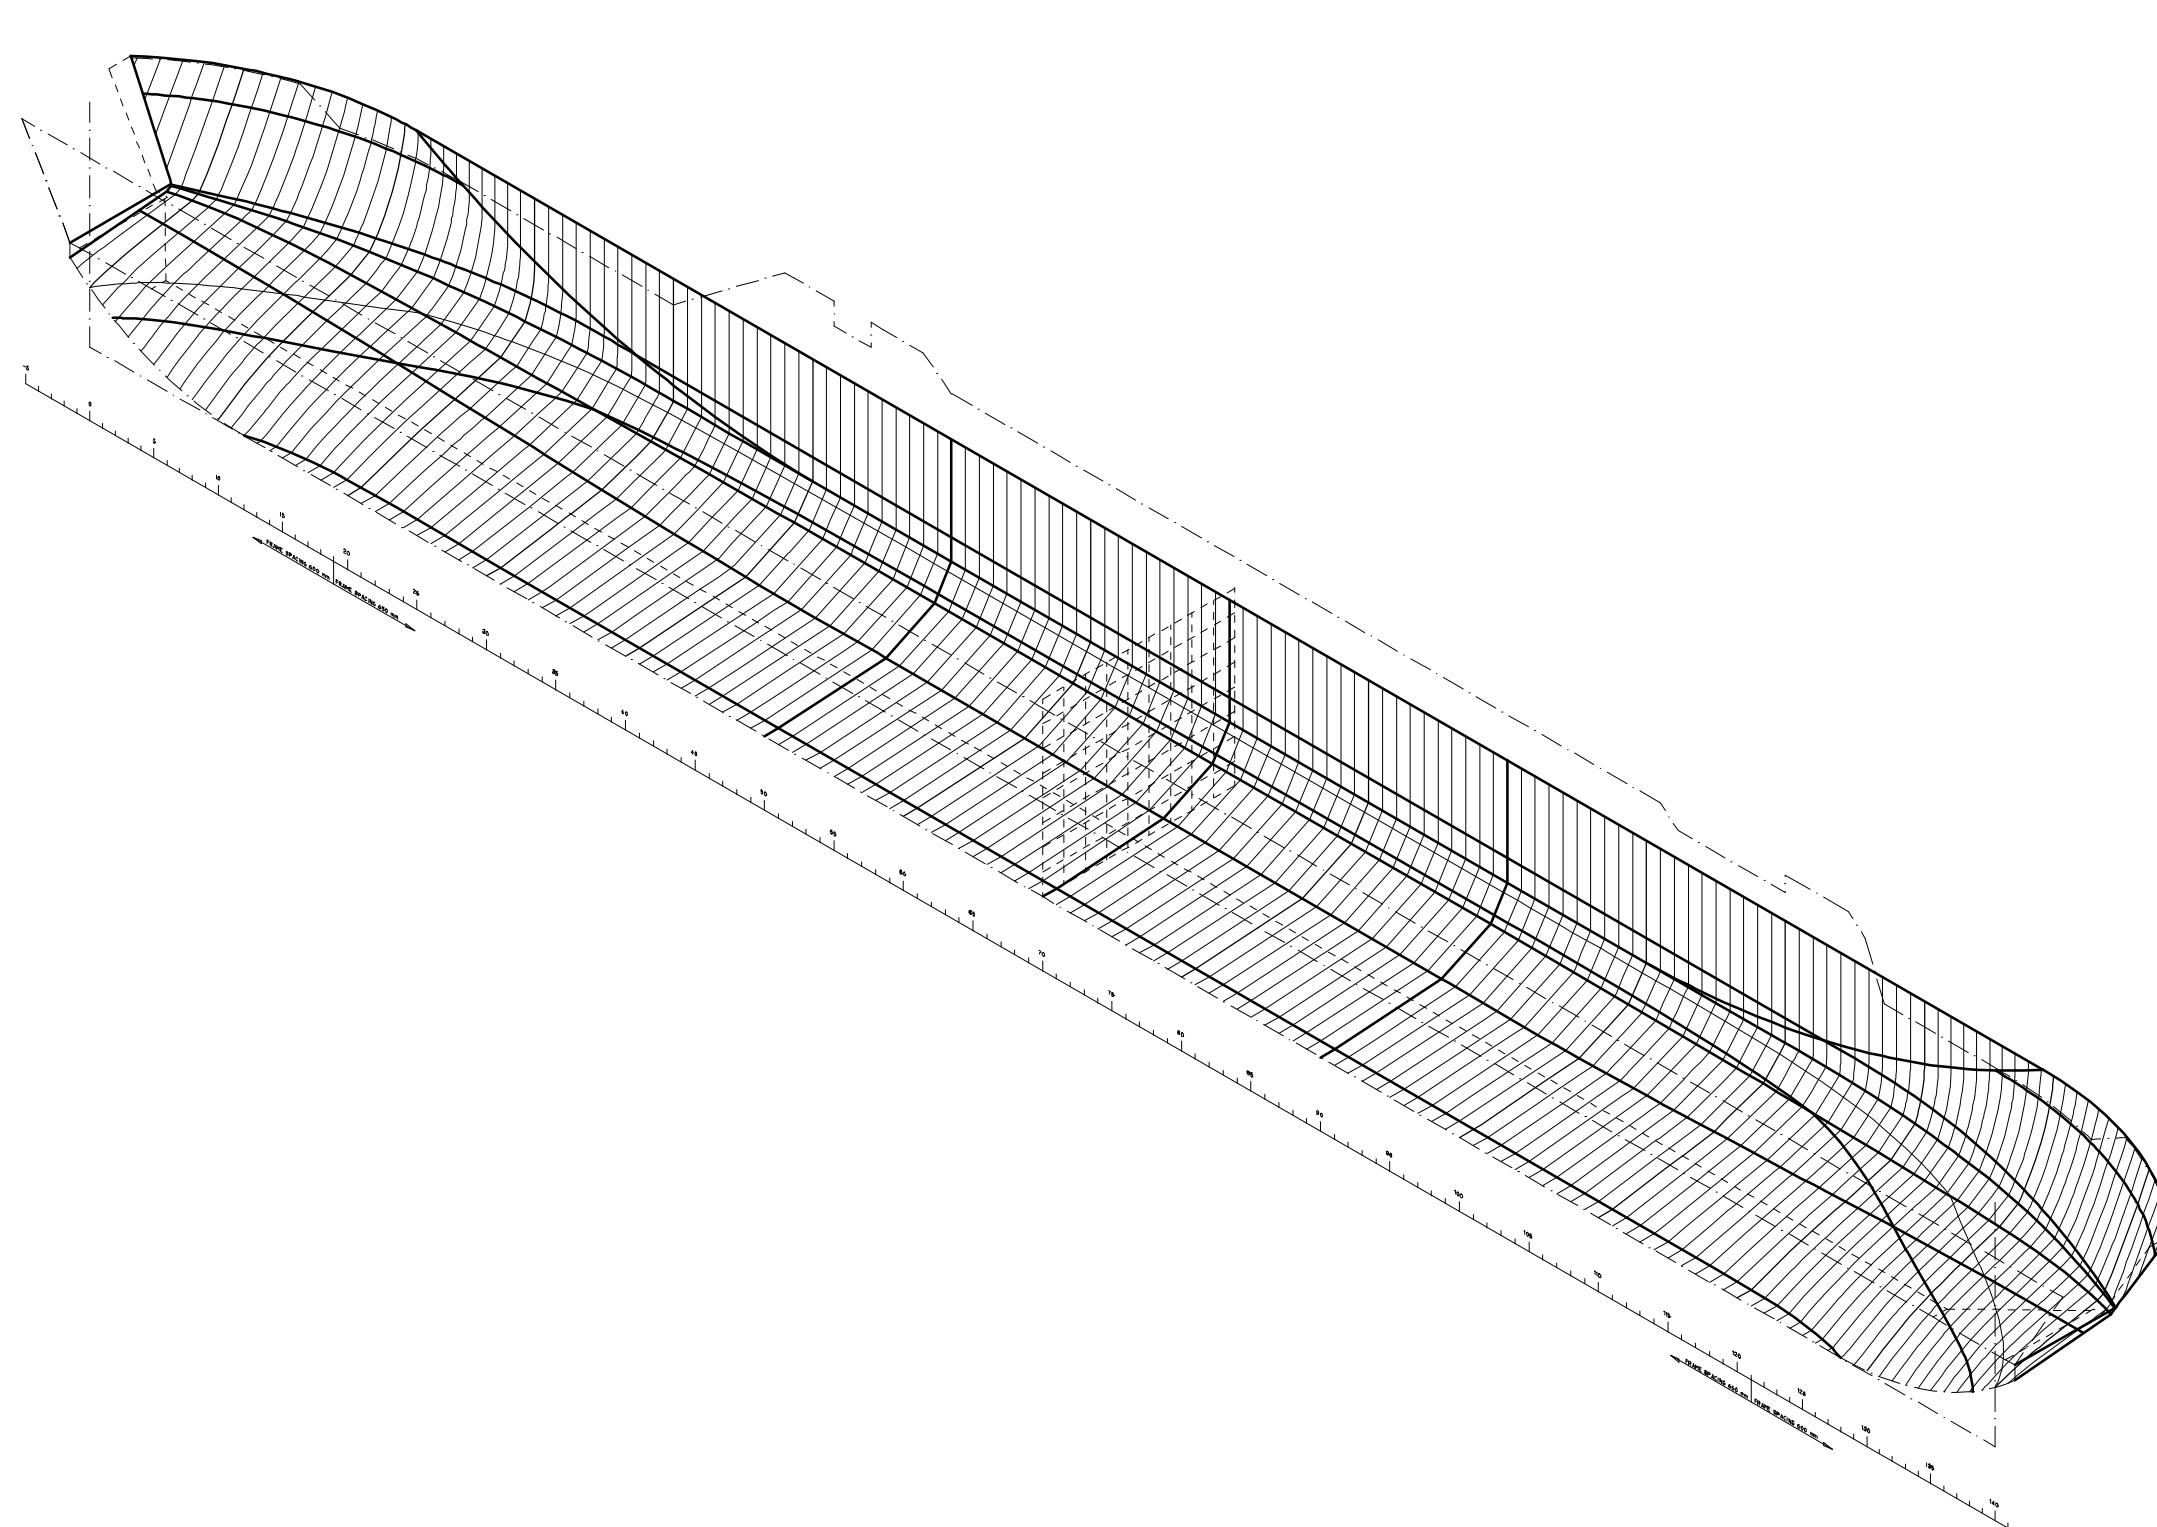
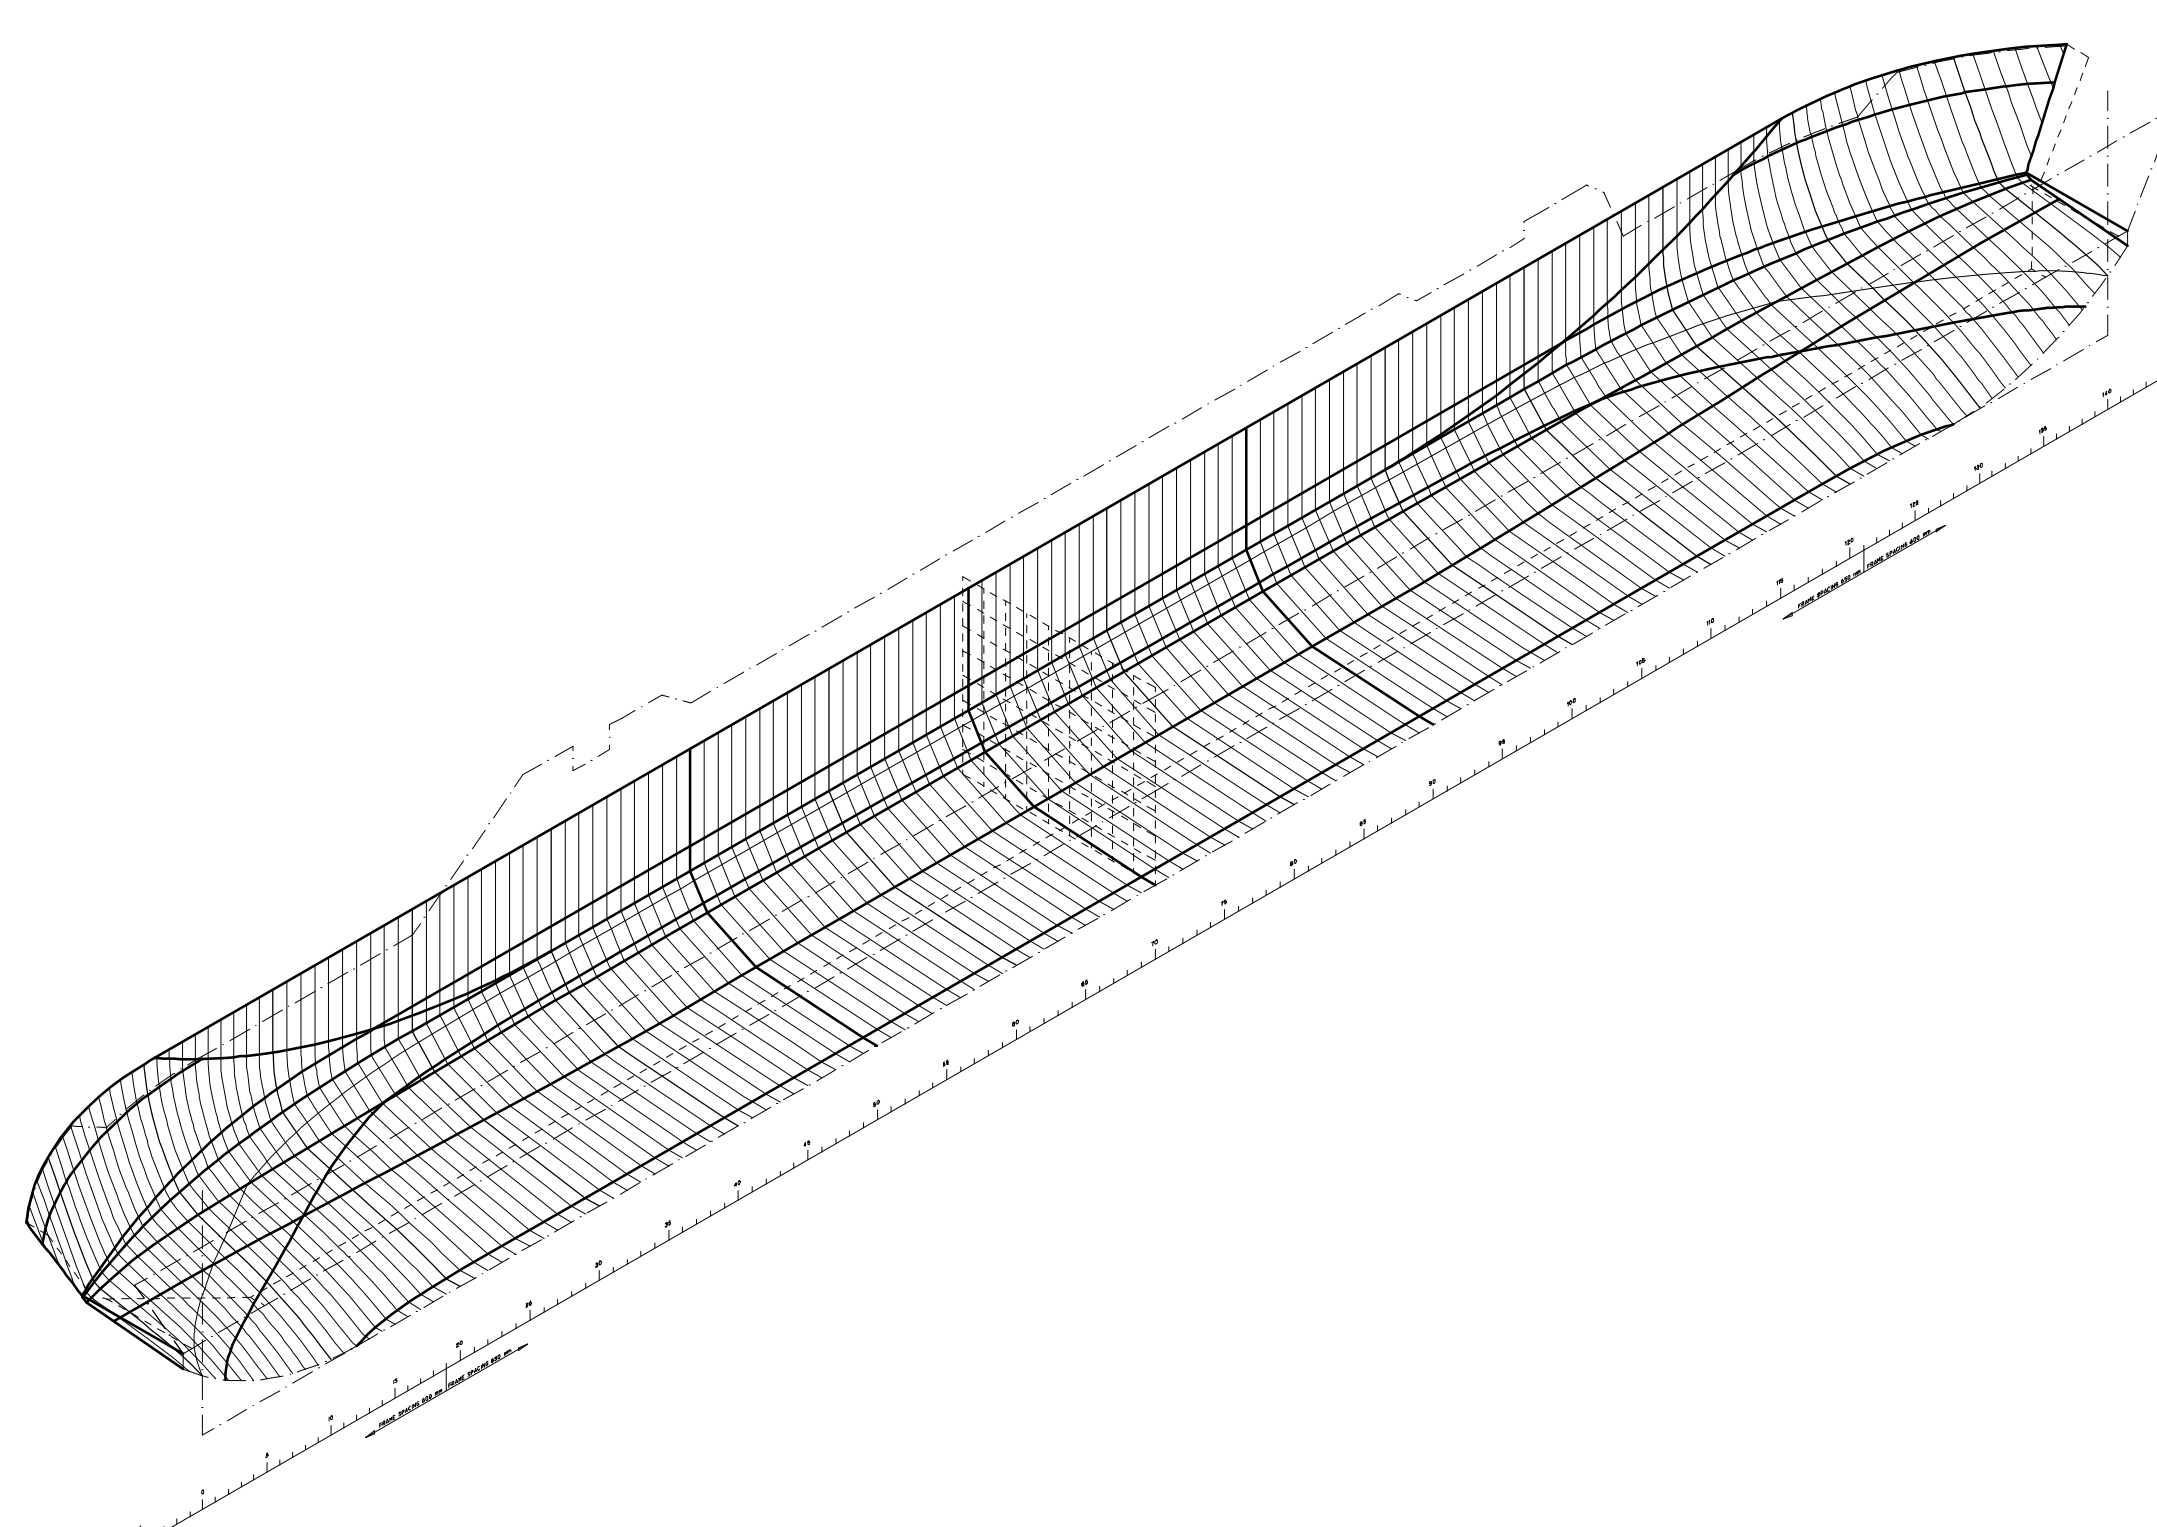


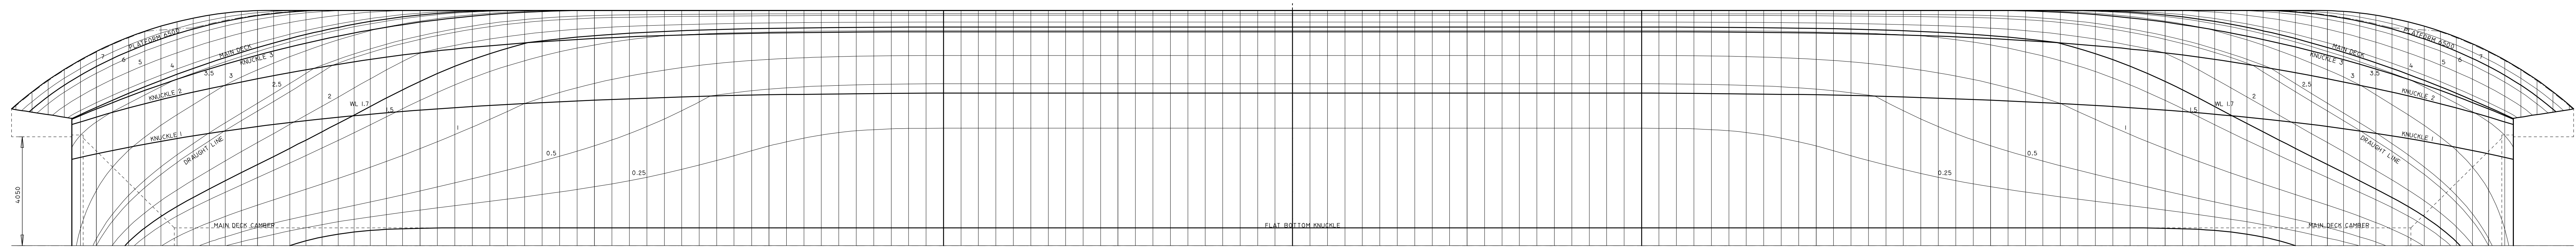

YARD No.	IMO No.
503	9703708
504	9703710
505	9703722
506	9703734

FRAME SPACING

FRAME -5 TO 19.....600 mm
FRAME 19 TO 121.....650 mm
FRAME 121 TO 145.....600 mm

MAIN DIMENSIONS

LENGTH overall obt.....	99.8 m
LENGTH between p.p.....	89.1 m
BREADTH moulded.....	17.5 m
DEPTH moulded.....	3.7 m
DRAUGHT scantling.....	2.4 m

[illegible]