Approval date: 11.06.2014/15:51:07
File name (PDM/UCM): 503-1420-1101391-o-1.pdf

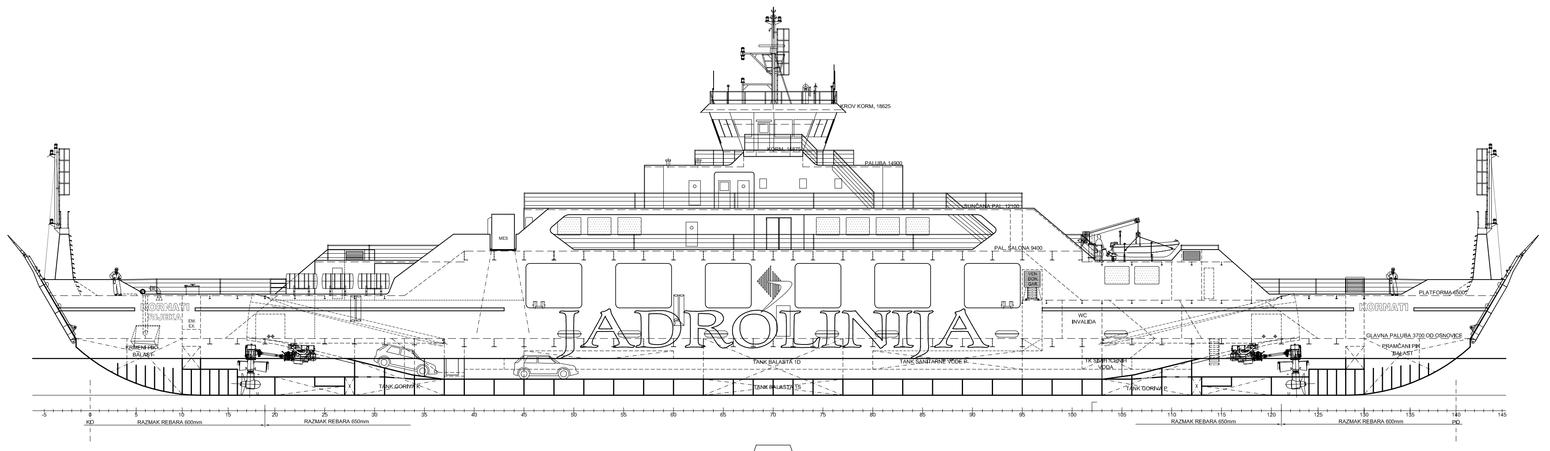

POPREČNI PRESJEK

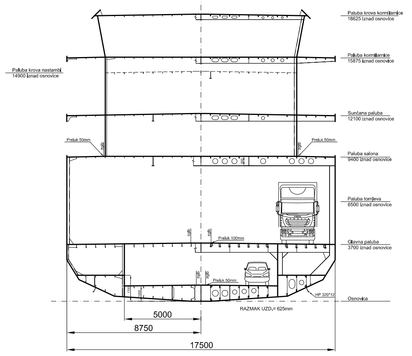

KORMILARNICA

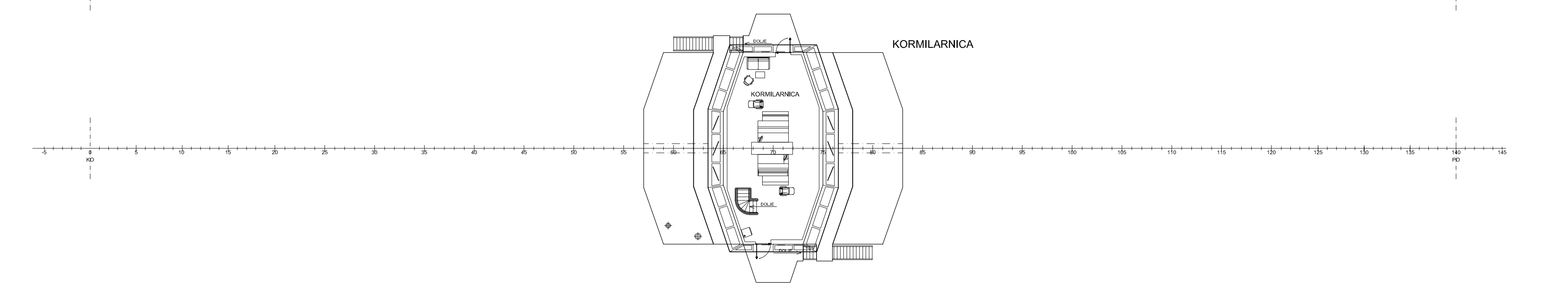

SUNČANA PALUBA

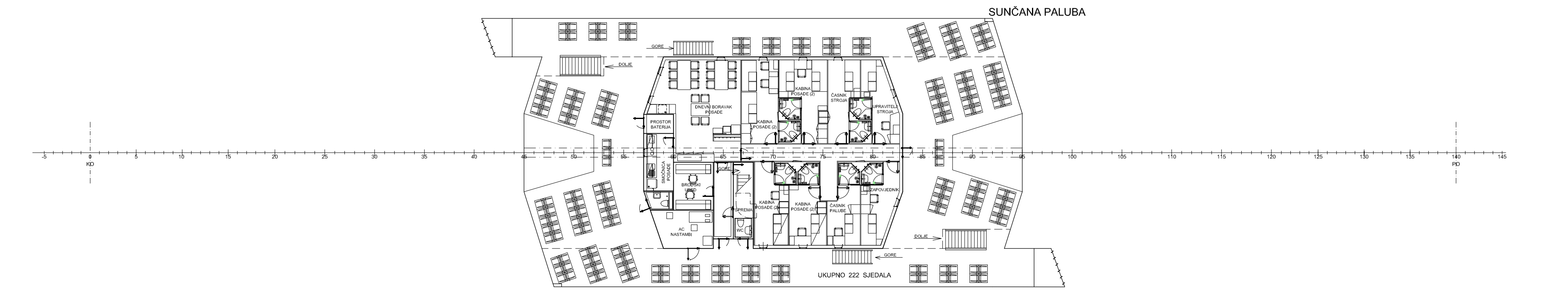

PALUBA SALONA

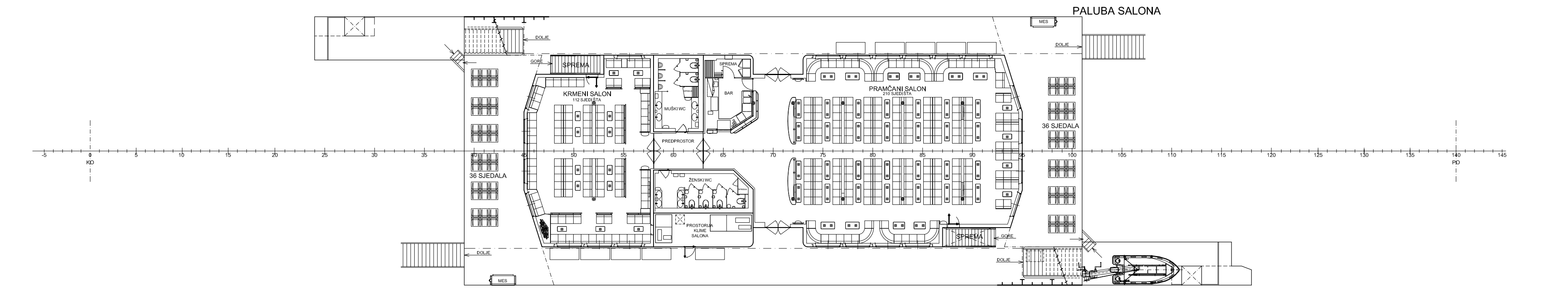

PALUBA PLATFORMI

GLAVNA PALUBA
111 automobila ili
16 tegljača

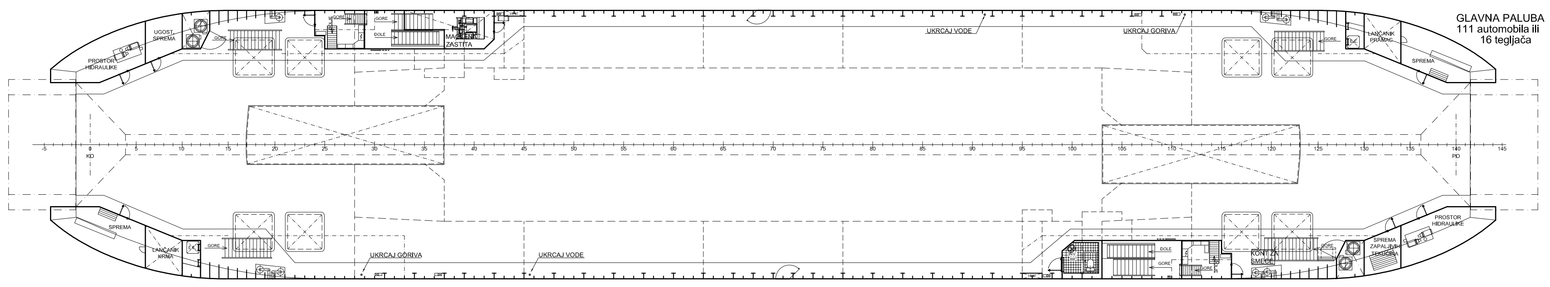

TANKOVI
34 automobila

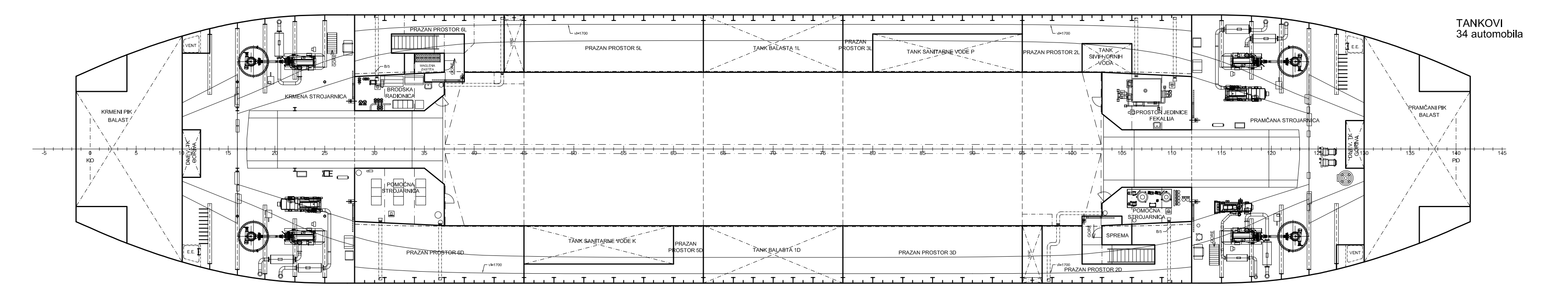

DVODNO

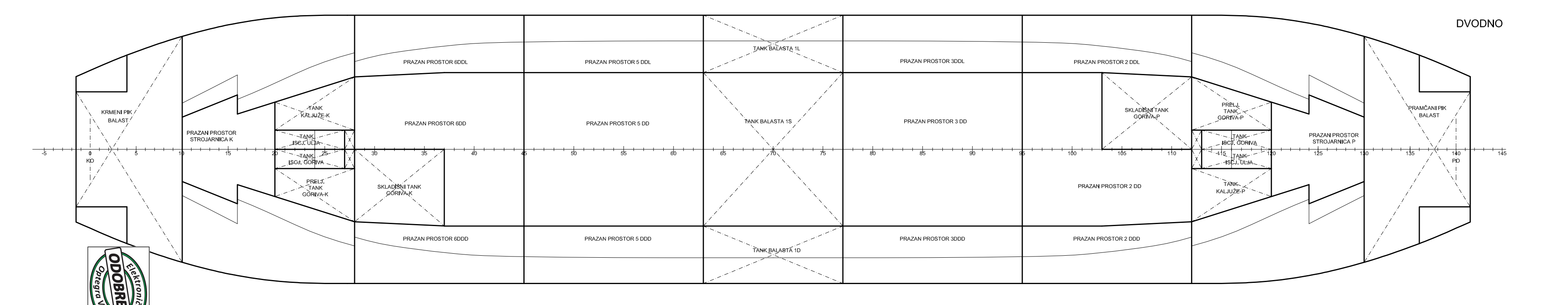

GL. KARAKTERISTIKE

DULJINA PREKO SVEGA	99,9	m
DULJINA IZMEDU OKOMICA	89,1	m
ŠIRINA	17,5	m
GAZ NA KVL	2,4	m
VISINA	3,7	m
ISTISNINA	2329	t
BRZINA (80%MCR)	12.28	kn

KAPACITET:

SJEDALA U PUTNIČKOM SALONU	322	kom
SJEDALA NA PALUBI SALONA	72	kom
SJEDALA NA SUNČANOJ PALUBI	222	kom
UKUPNI BROJ SJEDALA	616	kom
BROJ AUTOMOBILA NA GLAVNOJ PALUBI	111	kom
BROJ AUTOMOBILA U PODPALUBLJU	34	kom
UKUPNI BROJAUTOMOBILA	145	kom

RO-RO PUTNIČKI BROD
"KORNATI"

LUKA UPISA: RIJEKA
IMO BROJ: 9703708

OZNAKA KLASE:

HRB *50A1 Ro-ro putnički brod IWS M1 AUT 1, plovila u kategoriji D (područje plovidbe 6) trajanje putovanja do 90 minuta, opremljen za prijevoz upakiranih opasnih tereta klase 1 (eksplozivi), 2 (plinovi), 3 (zapaljive tekućine)

NARUČITELJ:

JADROLINIJA, društvo za linijski pomorski prijevoz putnika i tereta, Riva 16, Rijeka

GRADITELJ:

"ULJANIK" - Pula - Hrvatska

This drawing/document is property of ULJANIK JSC with all pertaining rights and it is not to be copied wholly or partially or used for any other purposes other than intended one without previous written permission of ULJANIK JSC who reserves all rights and interest thereto.

ULJANIK JSC
SALES AND PROJECTS
SHIPBUILDING PROJECTS Ltd
PULA, CROATIA

DESIGNED	M. CEROVAC
CONTROLLED	S. ŠPANIĆ dipl.ing.
CHECKED	M. BAJEC dipl.ing.
APPROVED	V. BUIĆ dipl.ing.

RO-RO PUTNIČKI BROD

SCALE	YARD N°:	SHEET	SHEETS
1:200	1101391 503	1	1

REVISION: A B C D E F G H
DATE: 11.06.2014.

ODOBRENO