


20						
19						
18						
17						
16						
15						
14						
13						
12						
11						
10	RESETKA KRILNA SKIDLJIVA S POKLOPCEM	800x315	2	SB 8314		
9	RESETKA KRILNA SKIDLJIVA TESKA	1000x500	8	SB 8319-A		
8	RESETKA KRILNA SKIDLJIVA TESKA	1000x800	4	SB 8319-A		
7	REGULACIJSKA ZAKLOPKA	500x500	4	Klimaoprema RZ 12-P		
6	REGULACIJSKA ZAKLOPKA	400x300	2	Klimaoprema RZ 12-P		
5	REGULACIJSKA ZAKLOPKA	650x500	2	Klimaoprema RZ 12-P		
4	AUTOM. PROTUPOZARNA ZAKLOPKA	1000x900	2		570261-2-035	
3	AUTOM. PROTUPOZARNA ZAKLOPKA	700x700 D=710	4		570261-2-031	
2	AKSIJALNI REVERZIBILNI VENTILATOR SE-12	Q=15000 m3/h Hst =570 Pa	2		574376-2-002	Dvobrzinski
1	AKSIJALNI TLACNI VENTILATOR S-11	Q=15000 m3/h Hst =570 Pa	2		574376-2-001	Dvobrzinski
Poz.	Naziv	Dimenzije	Kom.	Standard	Sist. Broj	Opaska

- NAPOMENA:1) Tankostijeni Kanali – pocincani lim debljine 1 mm spojen s prirubicama
Strukturni Kanali – celik obojani 3 mm ili vise
- 2) Maksimalna brzina zraka u ventilacionim kanalima je 12 m/s.
- 3) Svi ventilacioni ulazi i izlazi su daljinski upravljani iz kormilarnice.
- 4) Na svim otvorima u strojarnici biti ce postavljene zastitne mreze prema SB8523-D.
- 5) Upravljanje i indikacija ventilatora i zaklopki na mostu i gl. raz. ploci.

SIMBOLI:




KANAL PREMA GORE

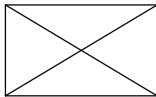

KANAL PREMA DOLJE




KANAL PREMA GORE I DOLJE

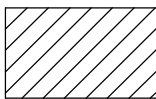

STRUKTURNI KANAL (debljina 3 mm ili vise)

S - TLACNI VENTILATOR
E - ODSISNI VENTILATOR
SE - REVERZIBILNI VENTILATOR

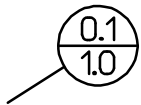

m² slobodna površina
m³/s kolicina zraka

ODOBRENO:	HRB
	VLASNIK

H	
G	
F	
E	
D	
C	
B	IZMIJENJENA POZ. 10 I DETALJ "A". DODANA NAPOMENA.
A	IZMIJENJENO PREMA ZAHTJEVU VLASNIKA.
ISSUE	ALTERATIONS


This drawing/document is property of Uljanik Brodogradiliste d.d. with all pertaining rights and it is not to be copied wholly or partially or used for any other purposes other than intended one without previous written permission of Uljanik Brodogradiliste who reserves all rights and interest thereto.

	ULJANIK SHIPYARD PULA - CROATIA	DESIGNED BY	Z. Poldrugo dipl. ing.	
		CONTROLLED	Z. Poldrugo dipl. ing.	
		CHECKED BY	M. Bajec dipl. ing.	
		APPROVED BY	D. Bilic dipl. ing.	


VENTILACIJA STROJARNICE PROJEKT													
MJERILO SCALE 1:100	2	5		8			GRADNJA BR. - YARD N ^o :				PAGES	LIST SHEET	LISTOVA SHEETS
	1	5	7	4	3	0	3	503, 504, 505, 506				5	1
MF: M	IZDANJE - ISSUE					A	B	C	D	E	F	G	H
	DATUM - DATE		16.05.2013.		23.07.13.	26.08.13.							

UZDUŽNI PRESJEK-LIJEVI BOK


KRMENA STROJARNICA

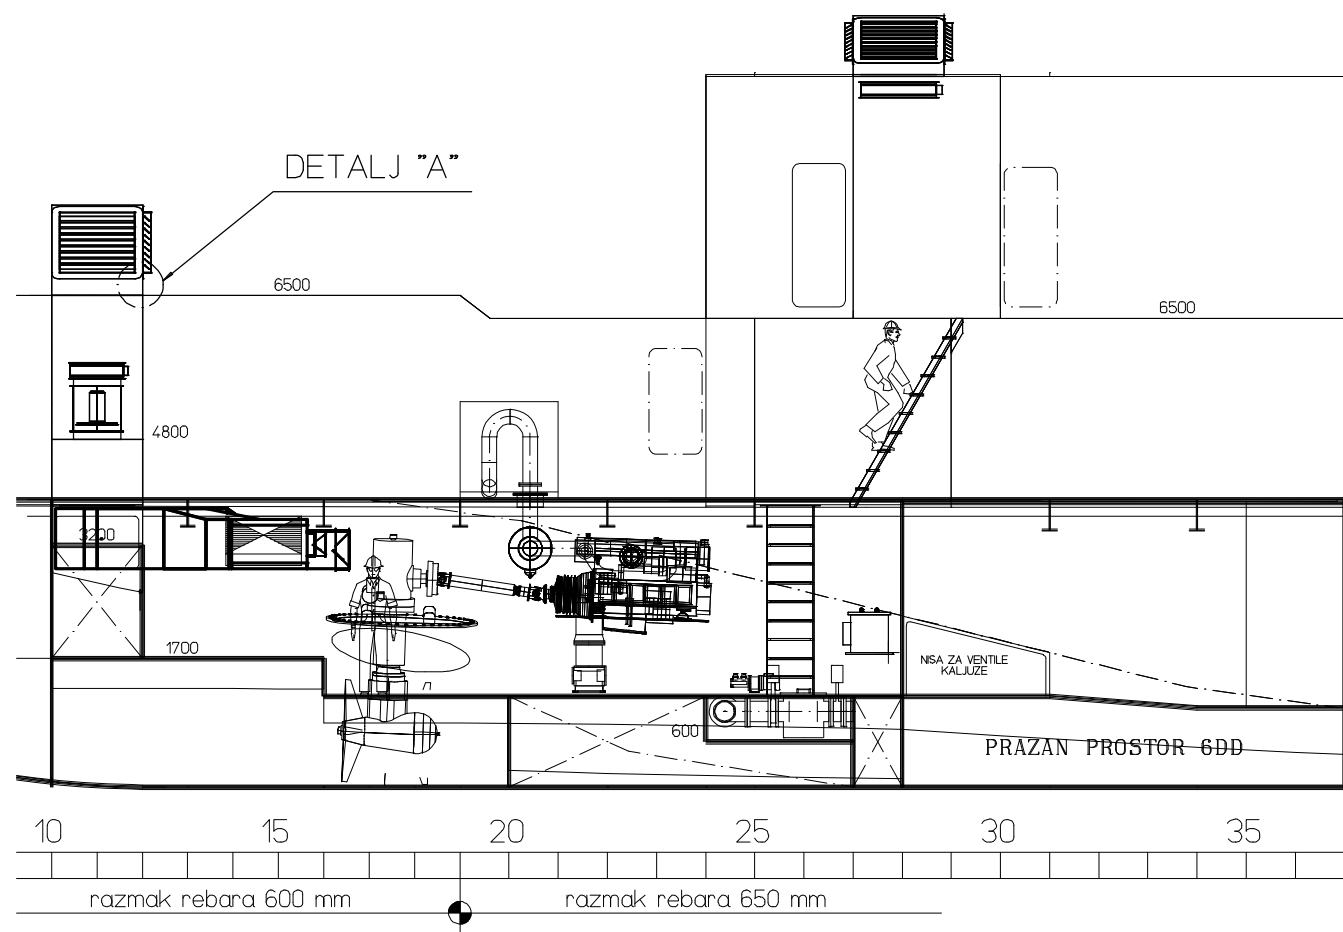

PRAMČANA STROJARNICA

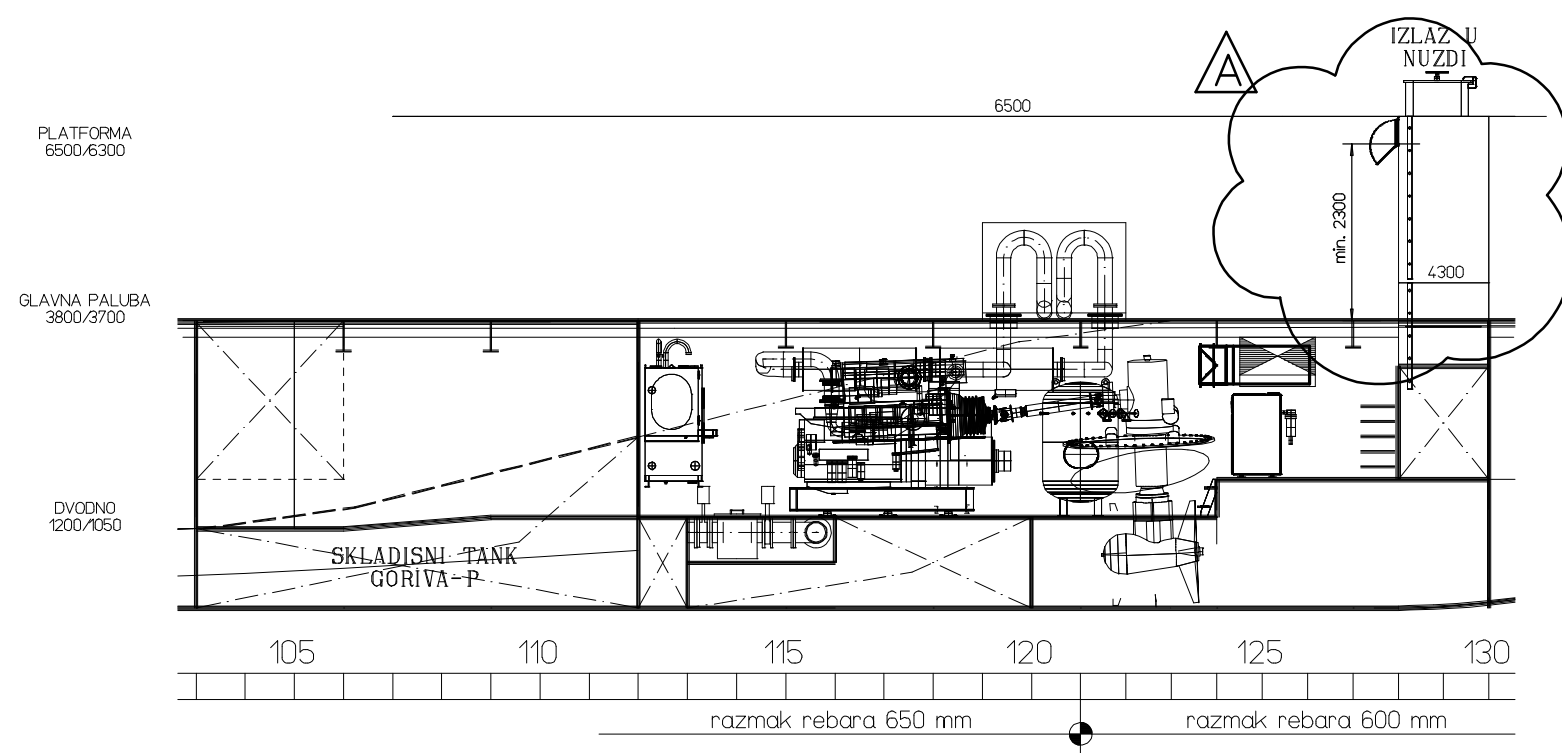

DETALJ "A"


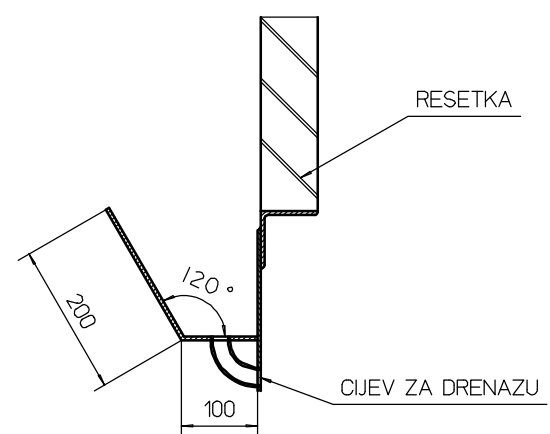


TLOCRT NA KROV DVODNA

KRMENA STROJARNICA

PRAMČANA STROJARNICA


Naziv datoteke (PDM/UCM): 503-1420-1574303-b-1.pdf

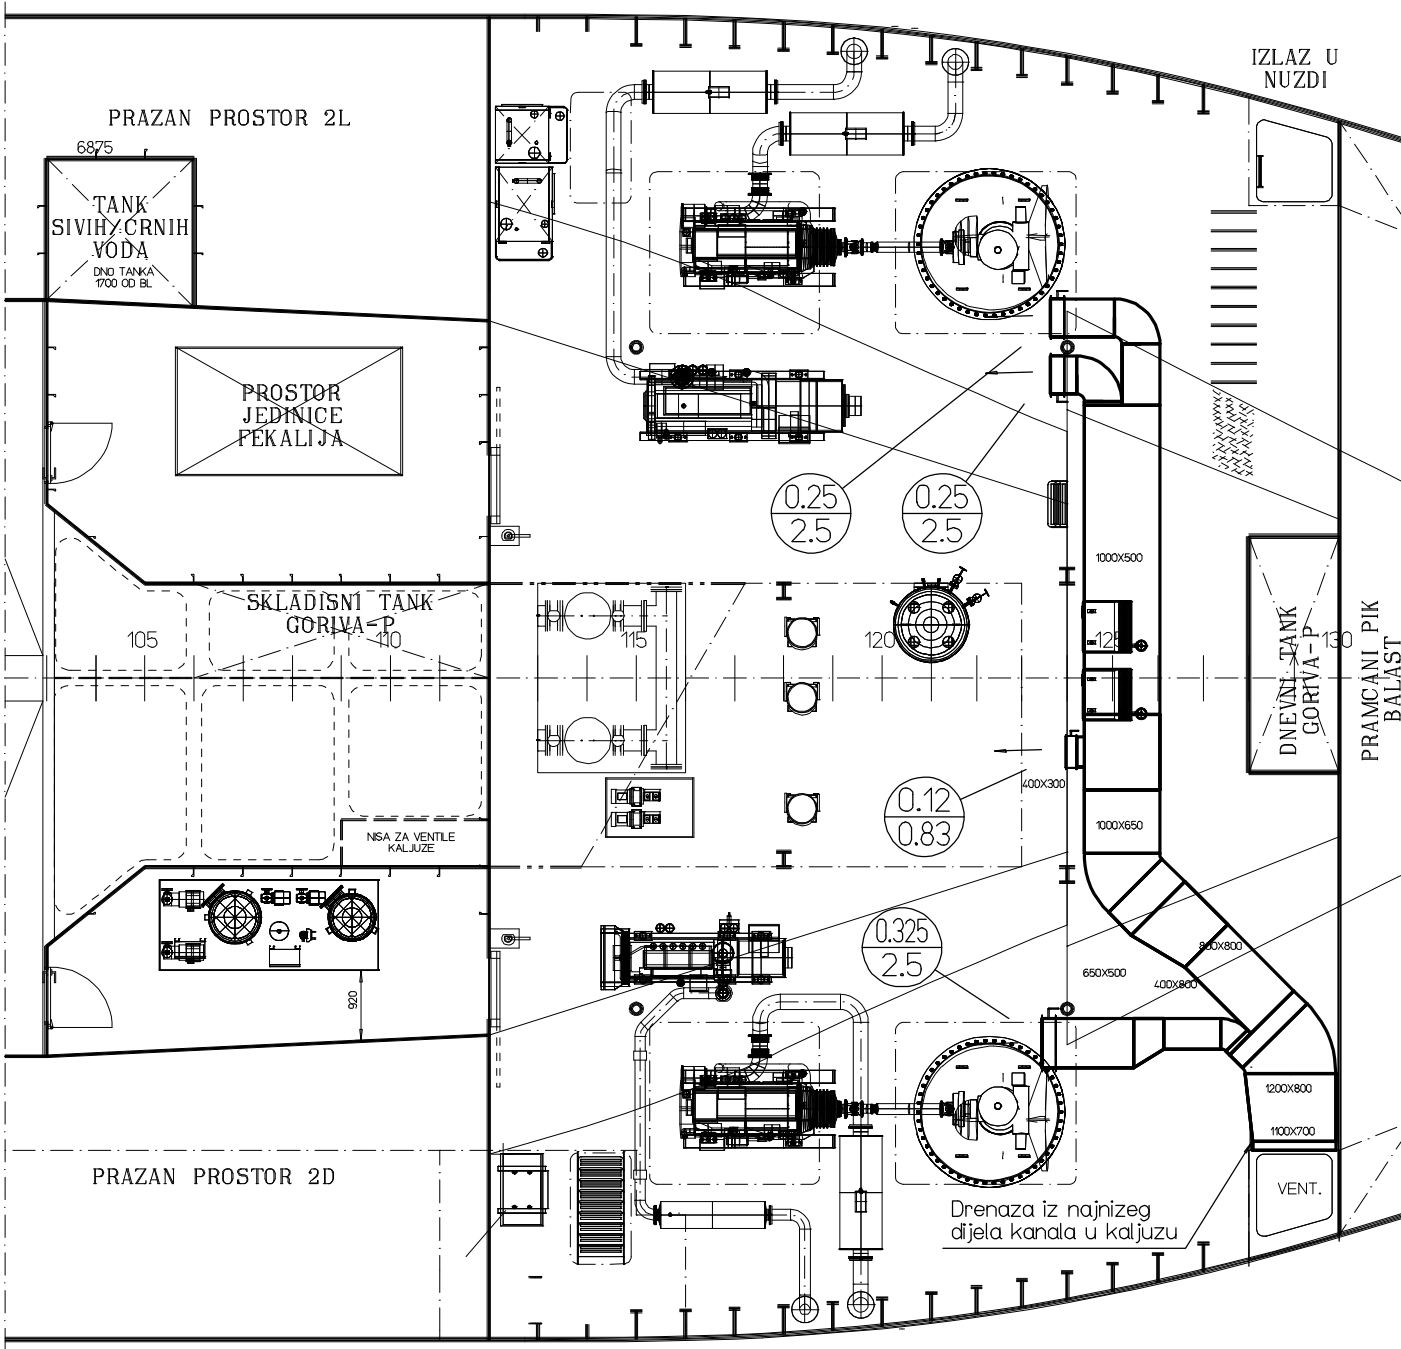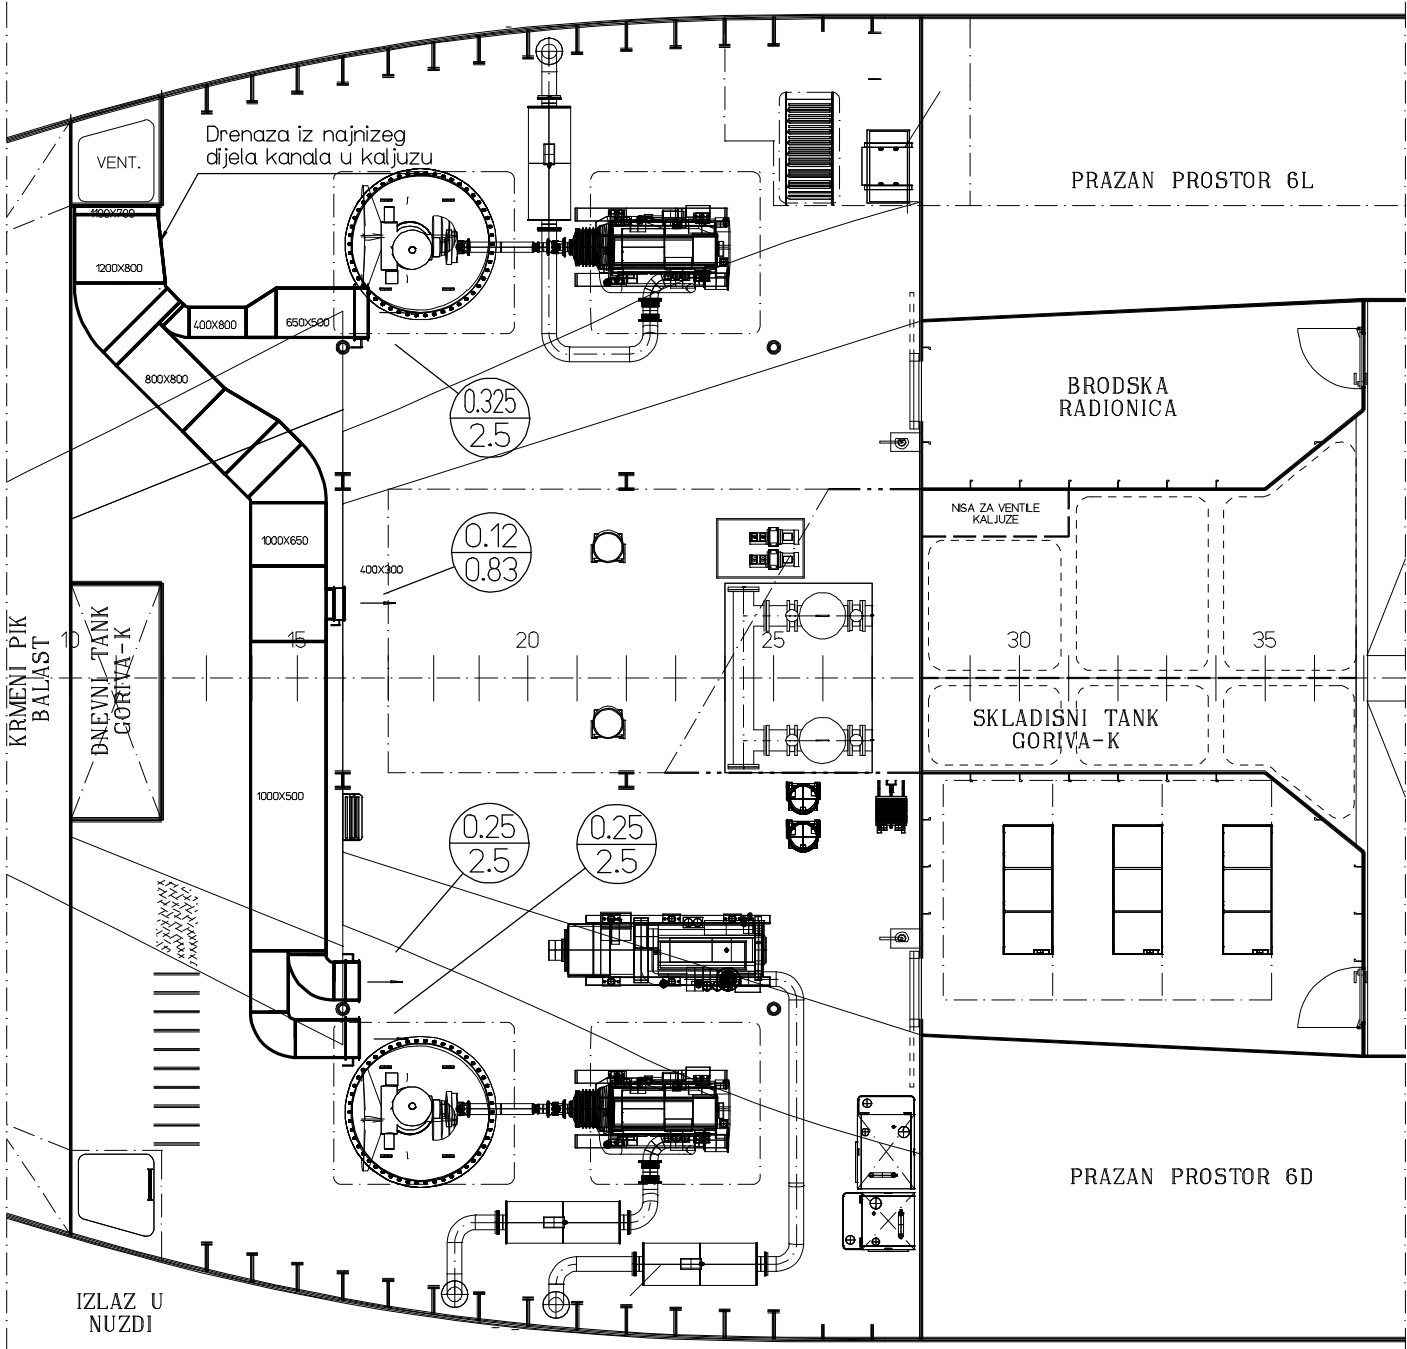



KRMENA STROJARNICA

PRAMČANA STROJARNICA


TLOCRT NA PLATFORMU

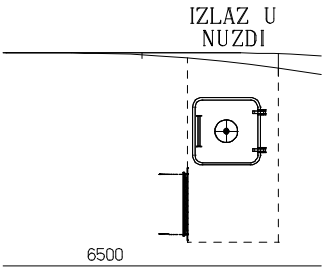


TLOCRT NA GLAVNU PALUBU

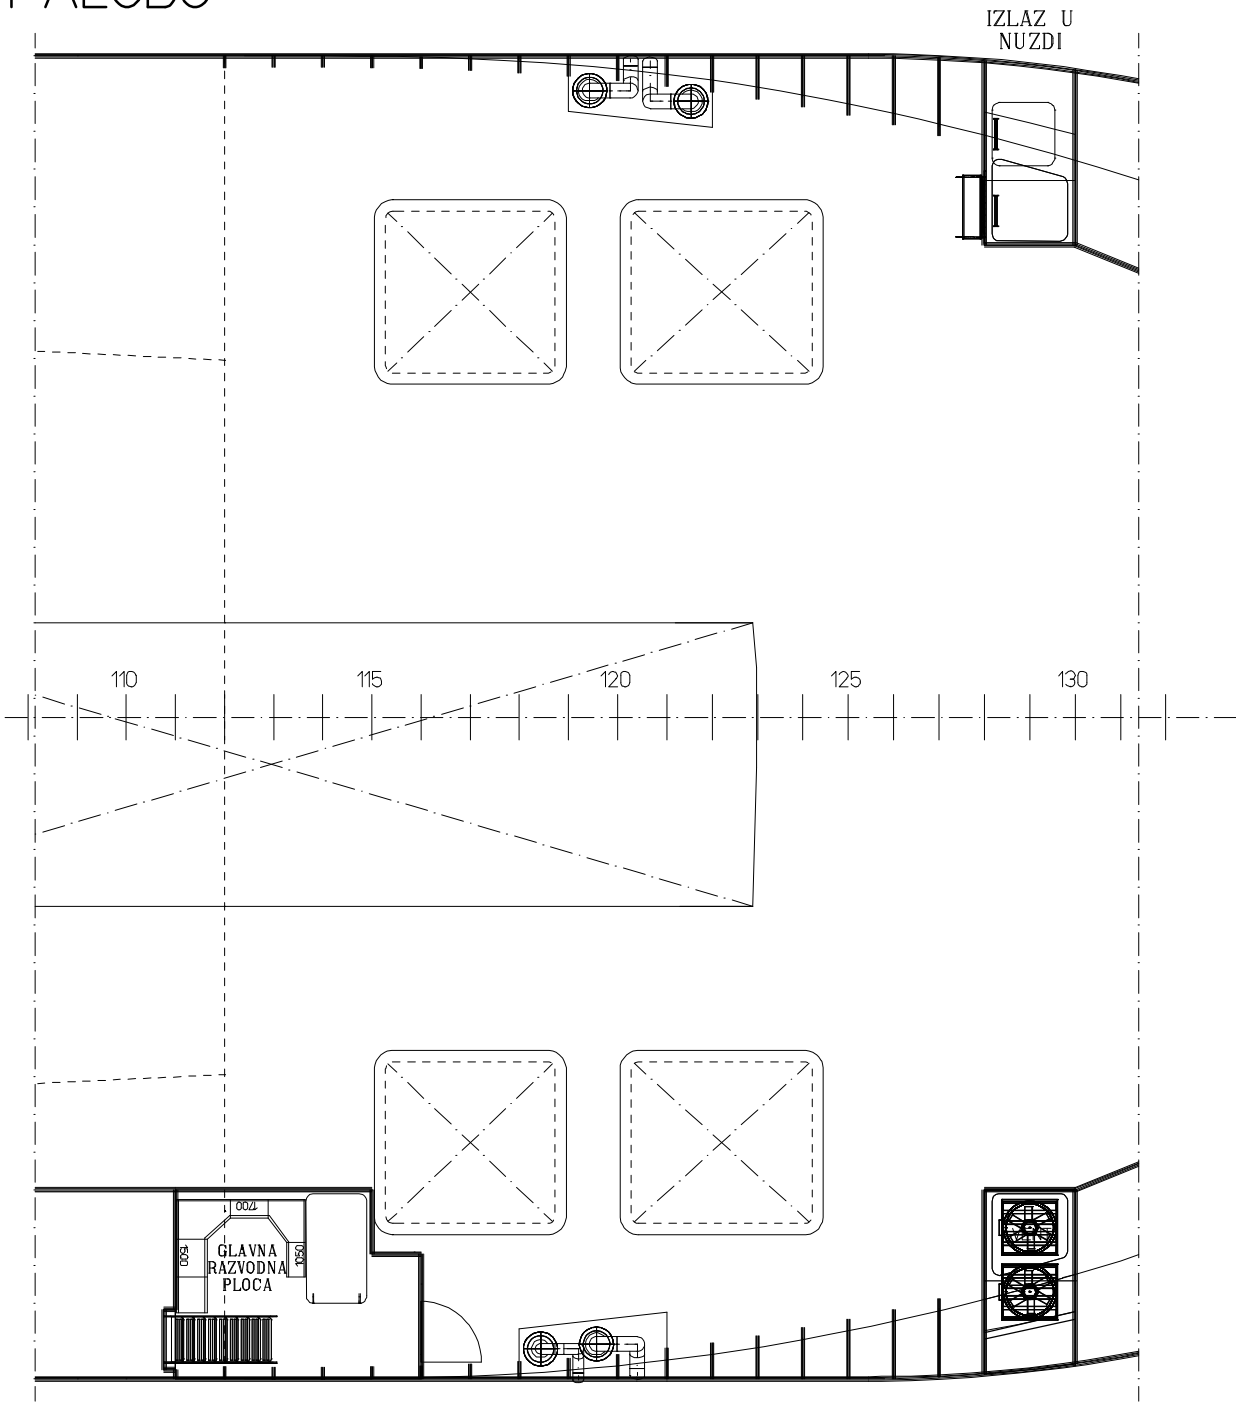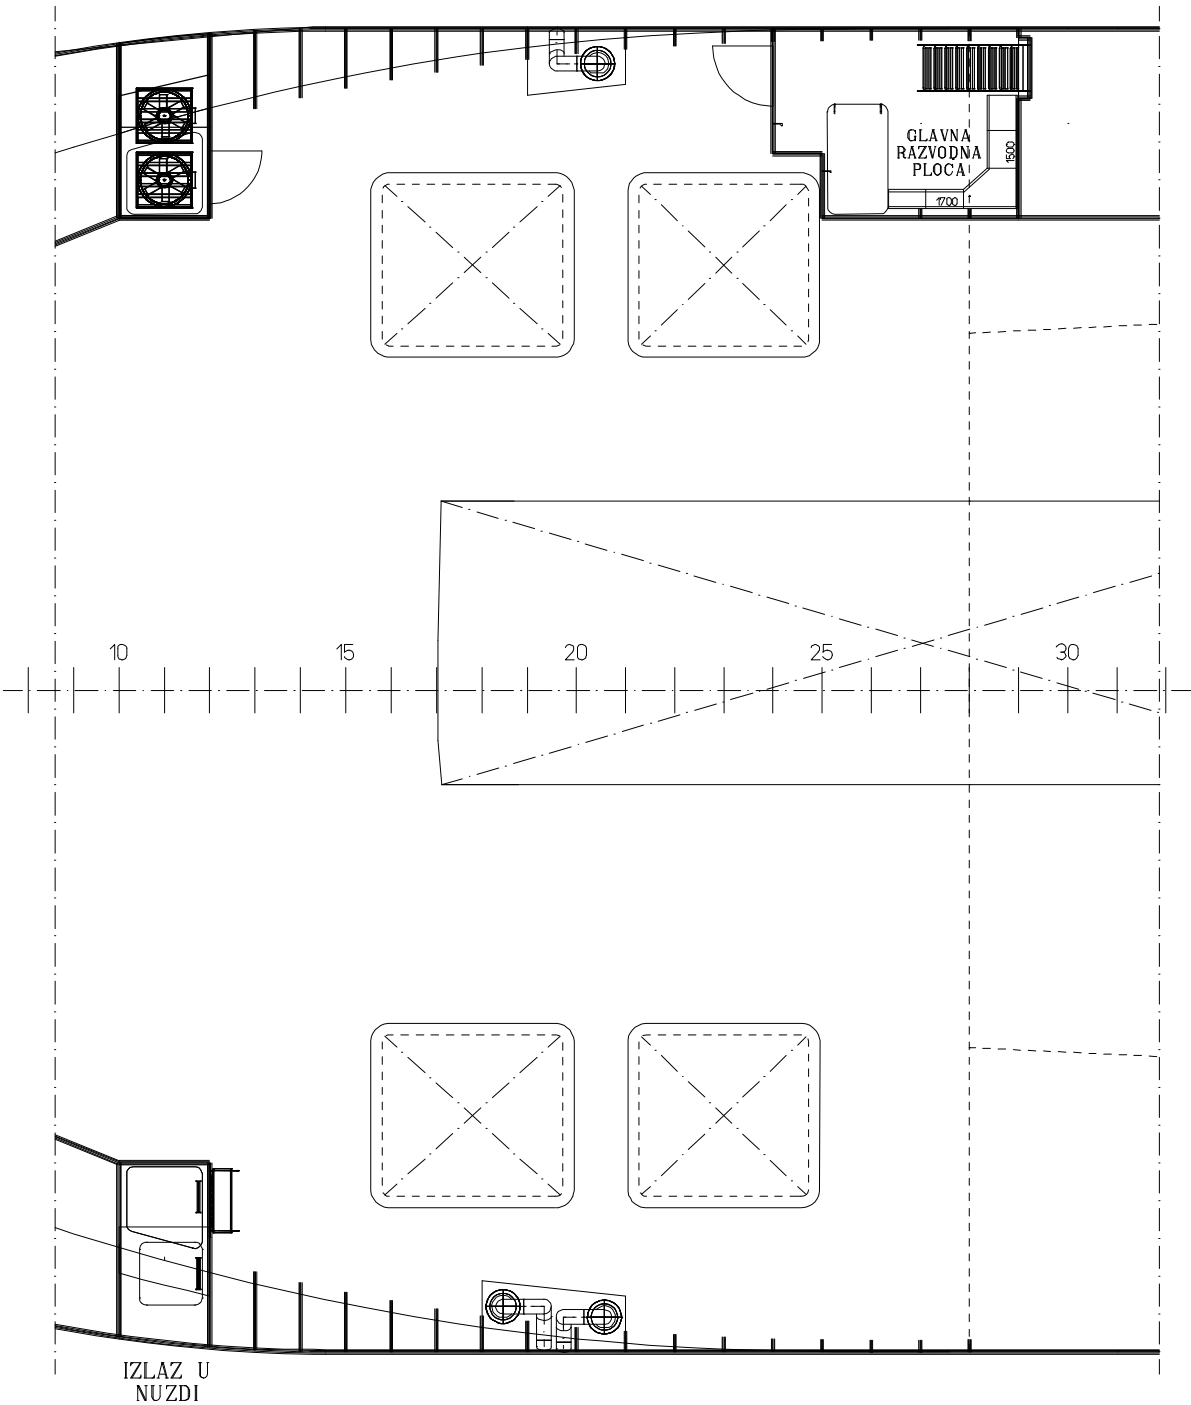


POPREČNI PRESJEK
R.16 PREMA KRMU

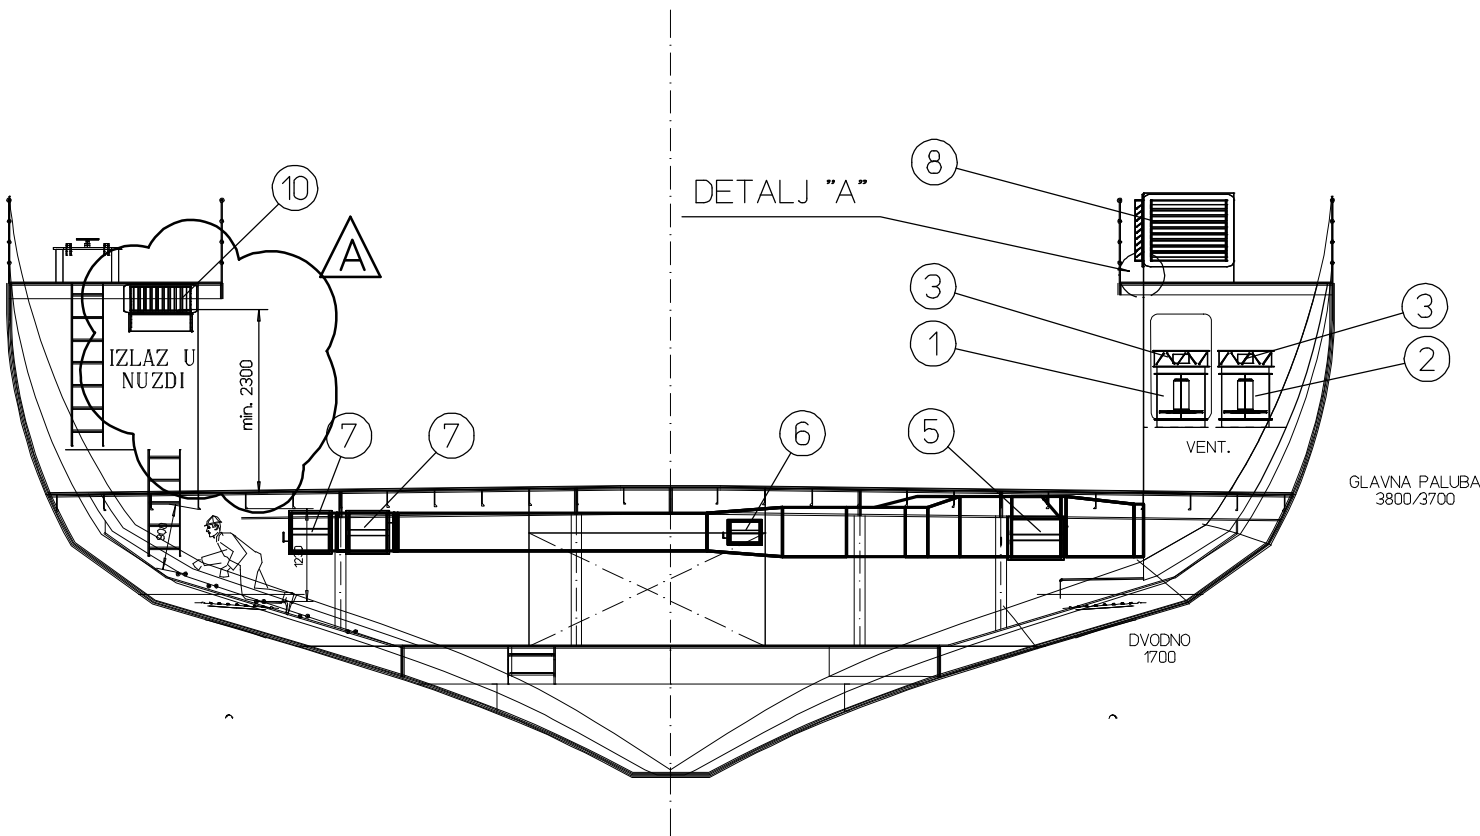

POPREČNI PRESJEK
R.22 PREMA PRAMCU

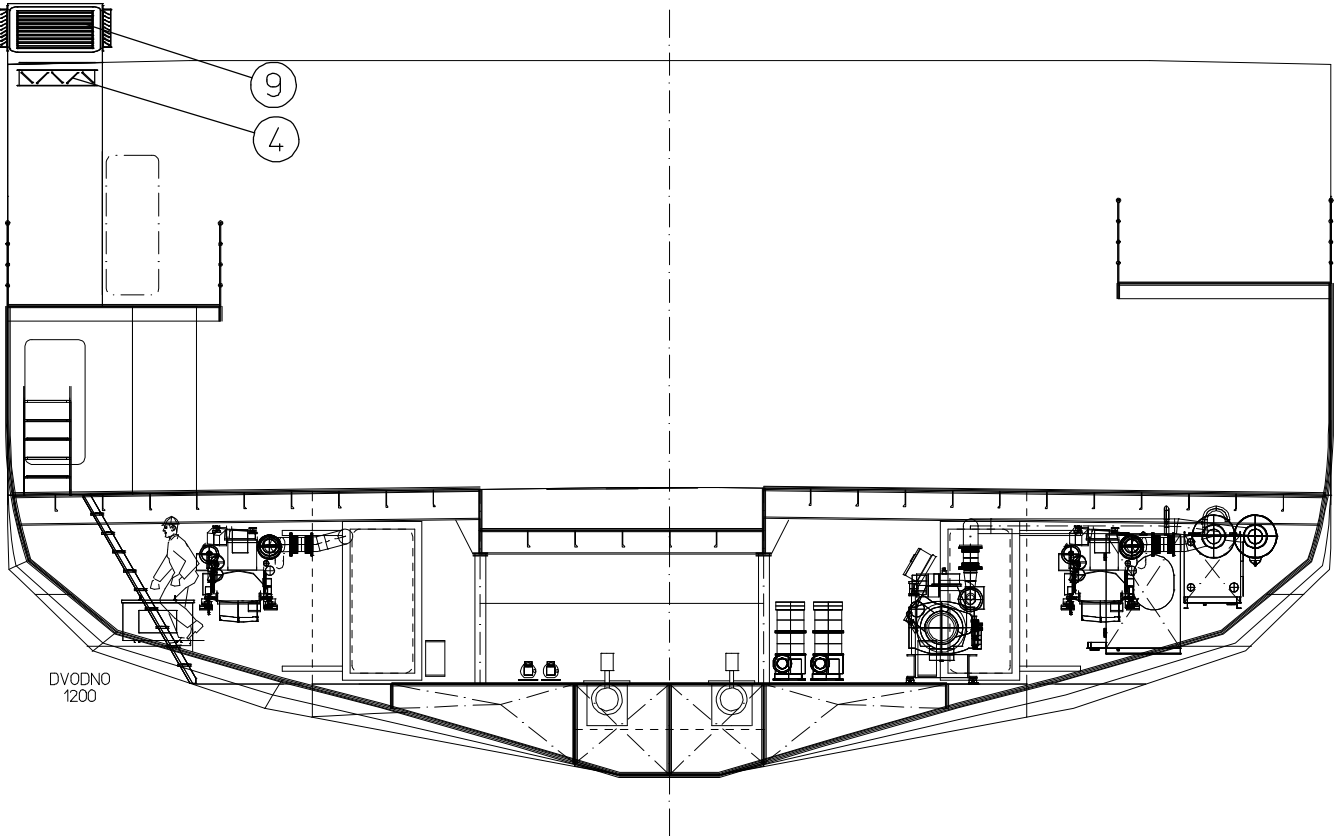

POPREČNI PRESJEK
R.16 PREMA PRAMCU

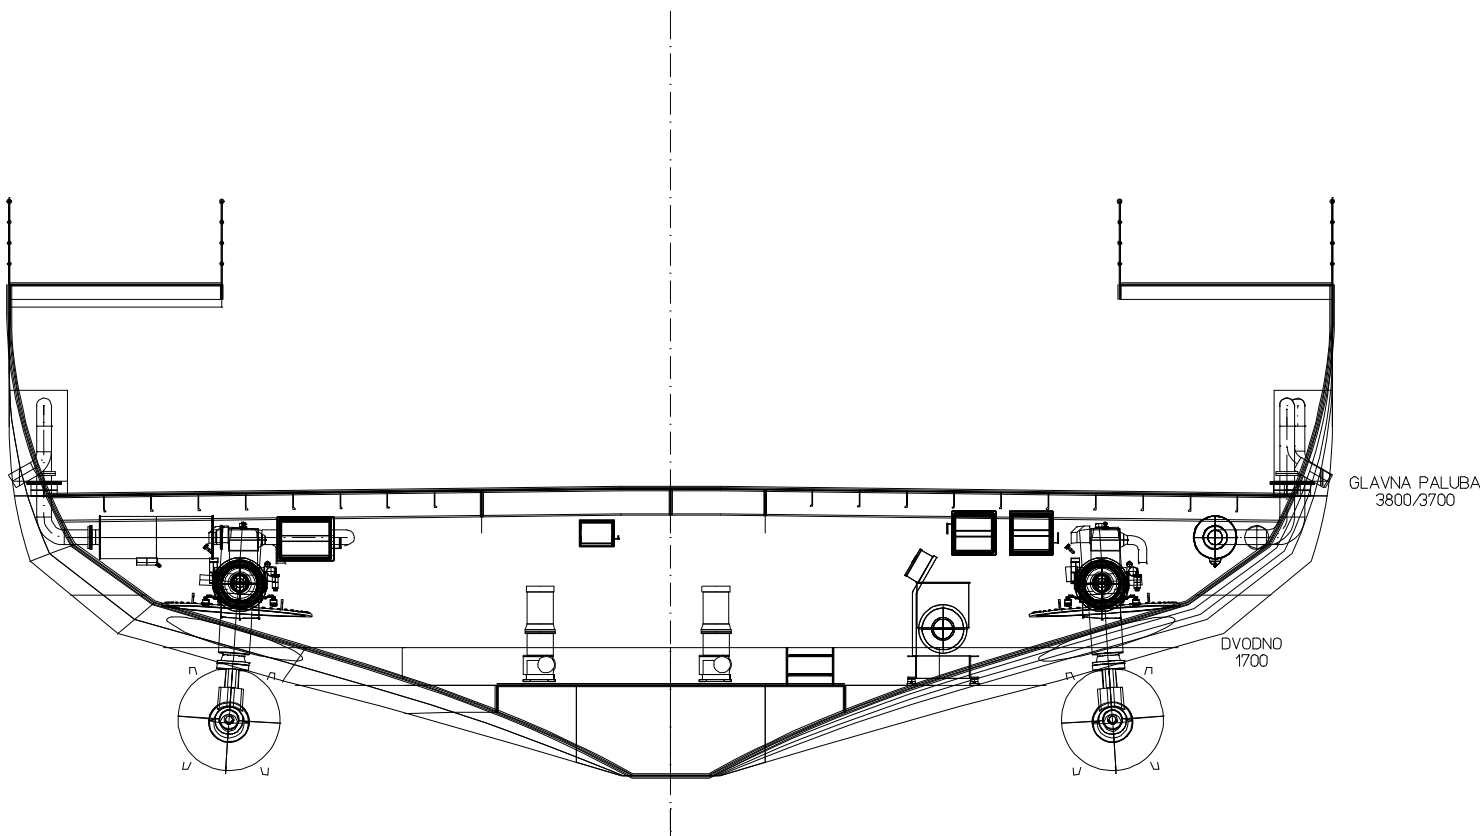

POPREČNI PRESJEK
R.28 PREMA PRAMCU

